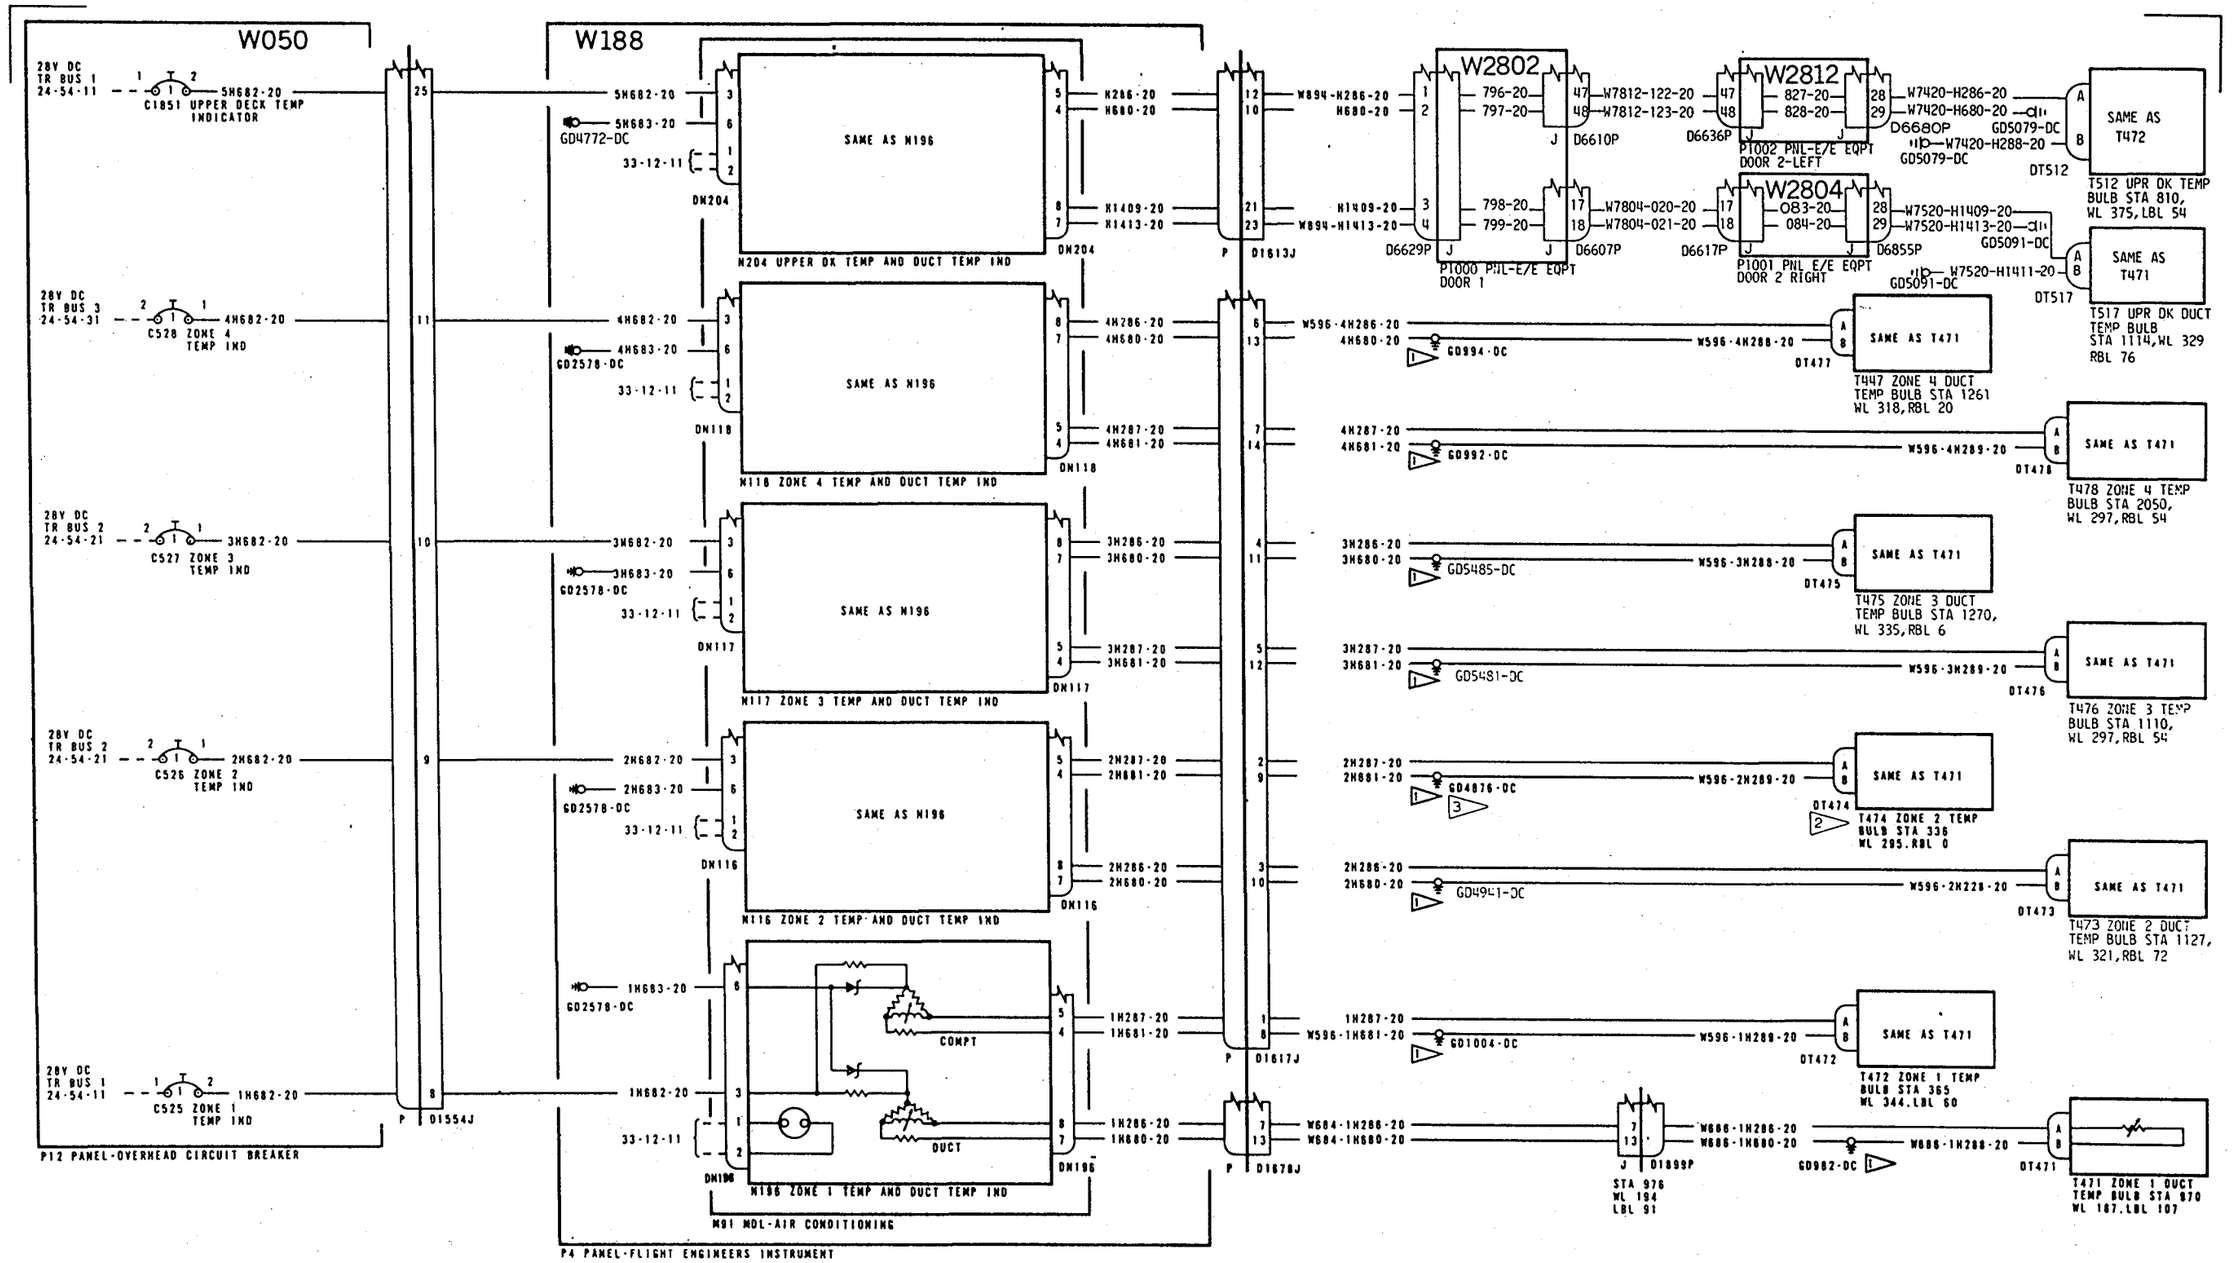


NOTES:
1. GROUND TO BE LOCATED NEAR TEMP BULB
2. T474 IS LOCATED AT STA 650, WL 295 RBL 54 FOR 163, 166, 170, 173, 176-179, 183-187, 189 (RS001-RS010, RS253-RS270)
3. GD4876-DC IS GD5741-DC FOR 163, 166 170, 173, 176-179, 183-187, 189 (RS001-RS010, RS253-RS270)

DRAFTED BY
CHECKED BY
DRAWING NO 61B74707
PAGE DATE JUN 6/88
DCN BS
CHANGE

21-65-11
PAGE 11

INDICATOR SYSTEM–ZONE AND ZONE DUCT TEMPERATURE

163, 166, 170, 173, 176-179, 183-187, 189, 212-213

RS251-RS270
RS001-RS010

21-65-11
PAGE 11