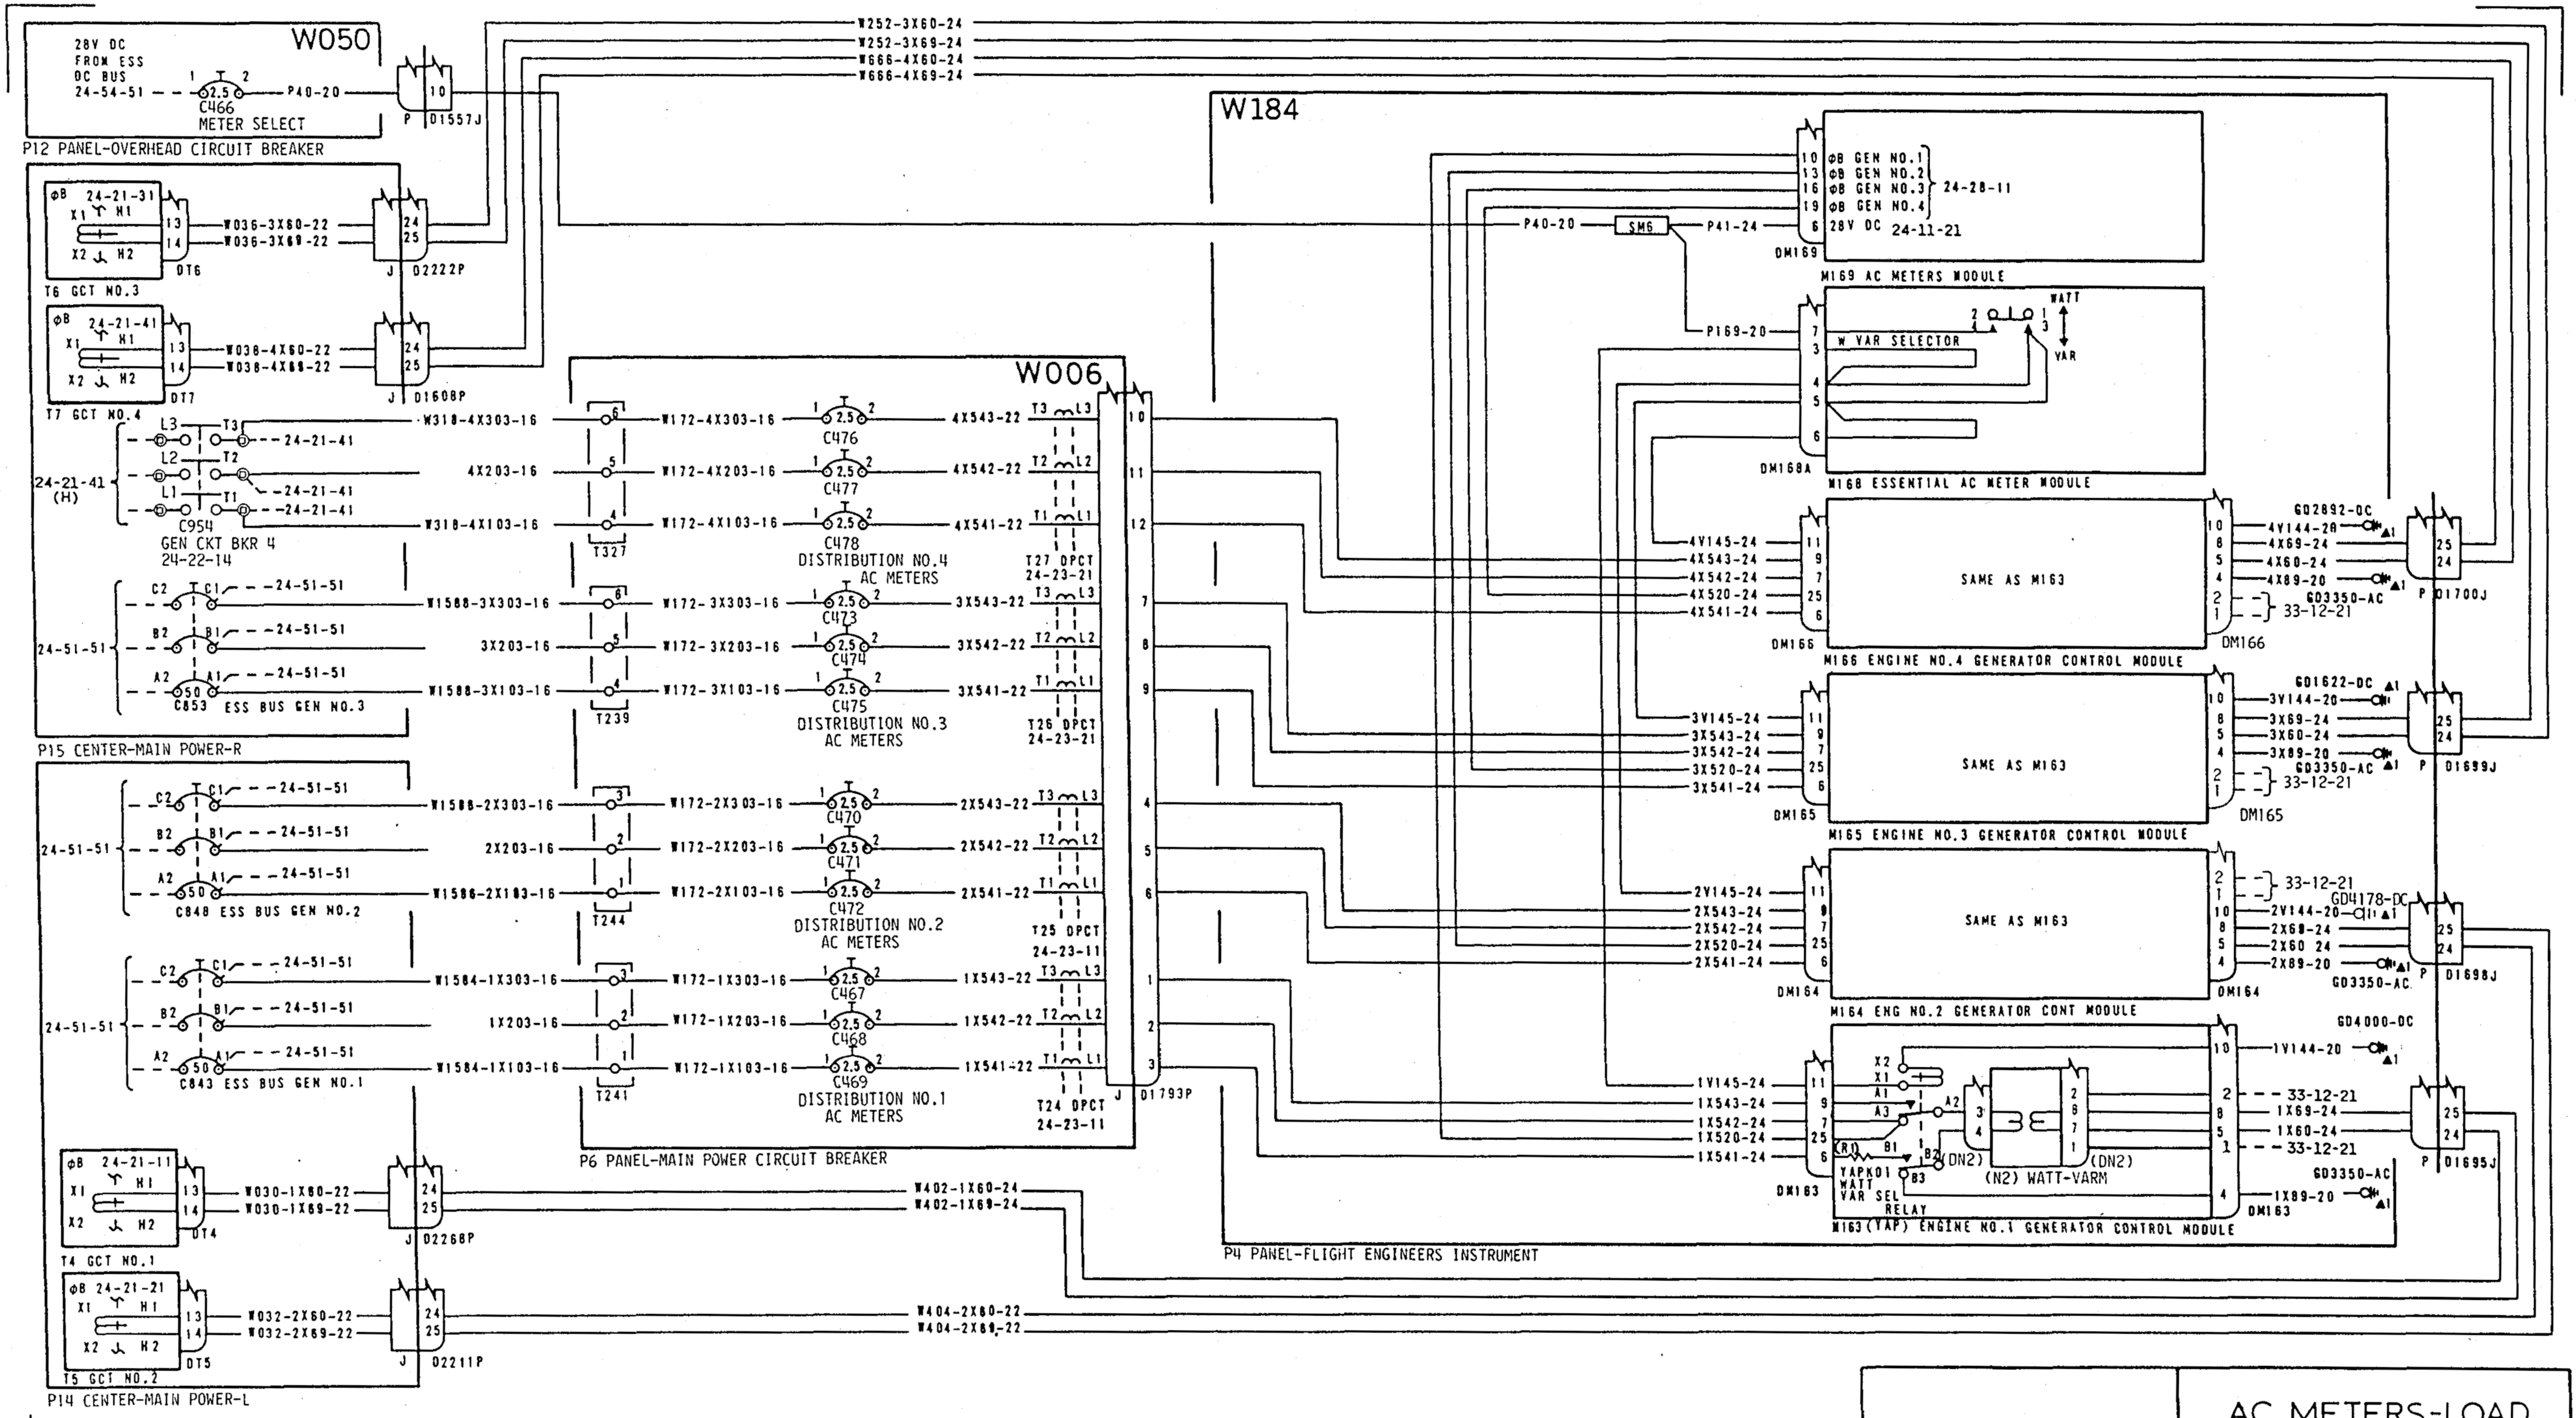

AC METERS-LOAD

149-150, 154-155, 161-163, 166, 169-170, 173, 176-179, 183-187, 189, 212-213

RD221-RD229
RS251-RS270
RS001-RS010

DRAFTED BY Craig Kjallin
CHECKED BY

DRAWING NO 61B74707
PAGE DATE: JUN 6/88

DCN: BS
CHANGE.